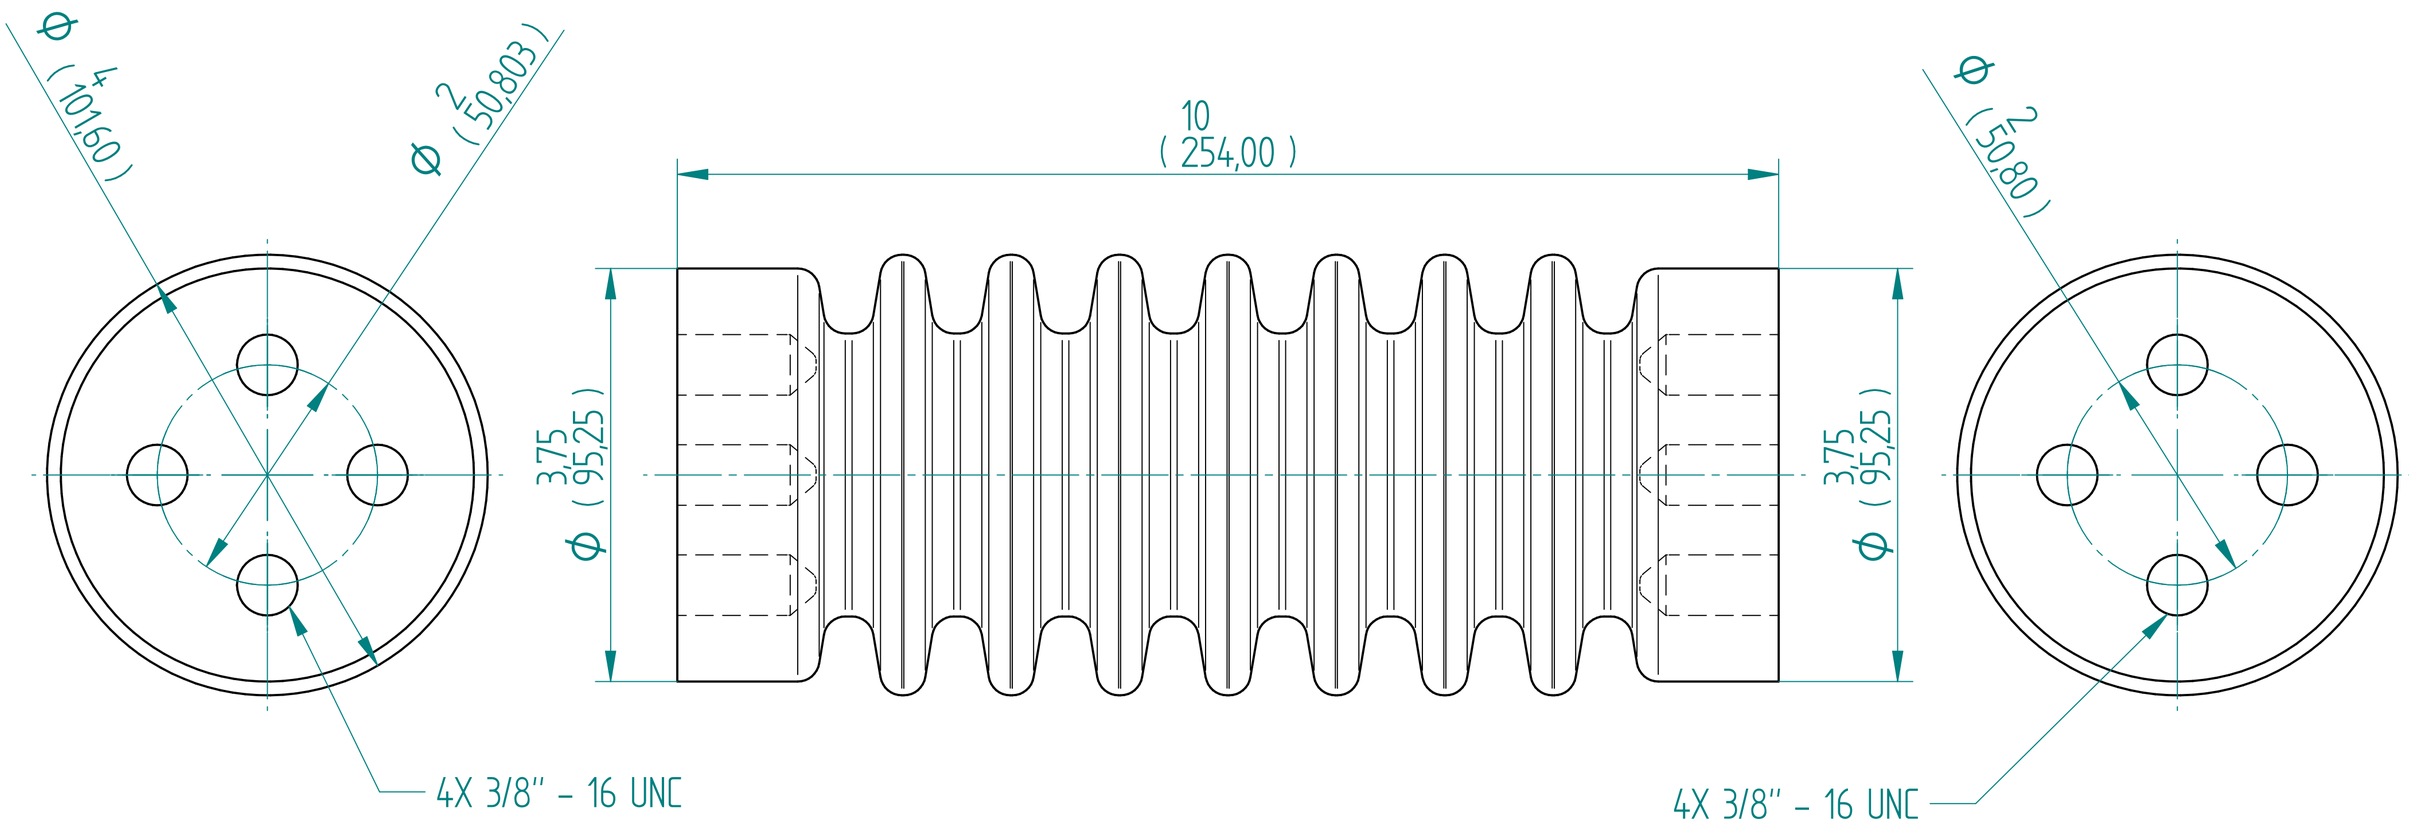


NOTE:
1. MATERIAL : EPOXY RESIN
2. RATED VOLTAGE : 25kV
3. CREEPAGE : >413MM
-FOR "BIL" RATINGS 95kV AND HIGHER, ALL INSERT CONFIGURATIONS WITH 3 OR MORE INSERTS ON EITHER END, WILL BE INTERNALLY CONNECTED (COMMON), ALLOWING FOR SELECTIVE APPLICATIONS.
-BREAK ALL SHARPS UNLESS OTHERWISE NOTED

THIRD ANGLE

STANDARD TOLERANCES UNLESS OTHERWISE SPECIFIED		
	LINEAR DIMENSION	0.5 UP TO 3 ± 0.1 OVER 3 UP TO 6 ± 0.5 OVER 6 UP TO 30 ± 1 OVER 30 UP TO 120 ±1.5 OVER 120 UP TO 400 ± 2.5 OVER 400 UP TO 1000 ± 4
	HOLE DIAMETER	1 UP TO 6 ± 0.5 OVER 6 UP TO 12 ± 0.5 OVER 12 ± 1
	ANGLES	DIMENSIONED ± 1° UNDIMENSIONED 90° ± 2°

ACCRETION POWER

DRN BY	CHD BY	DATE	
PRP	C.P.P	04.11.2025	SCALE
			NTS

TITLE.
25KV STANDOFF INSULATOR

DRG NO.
NEIS-E-25-003

REV A